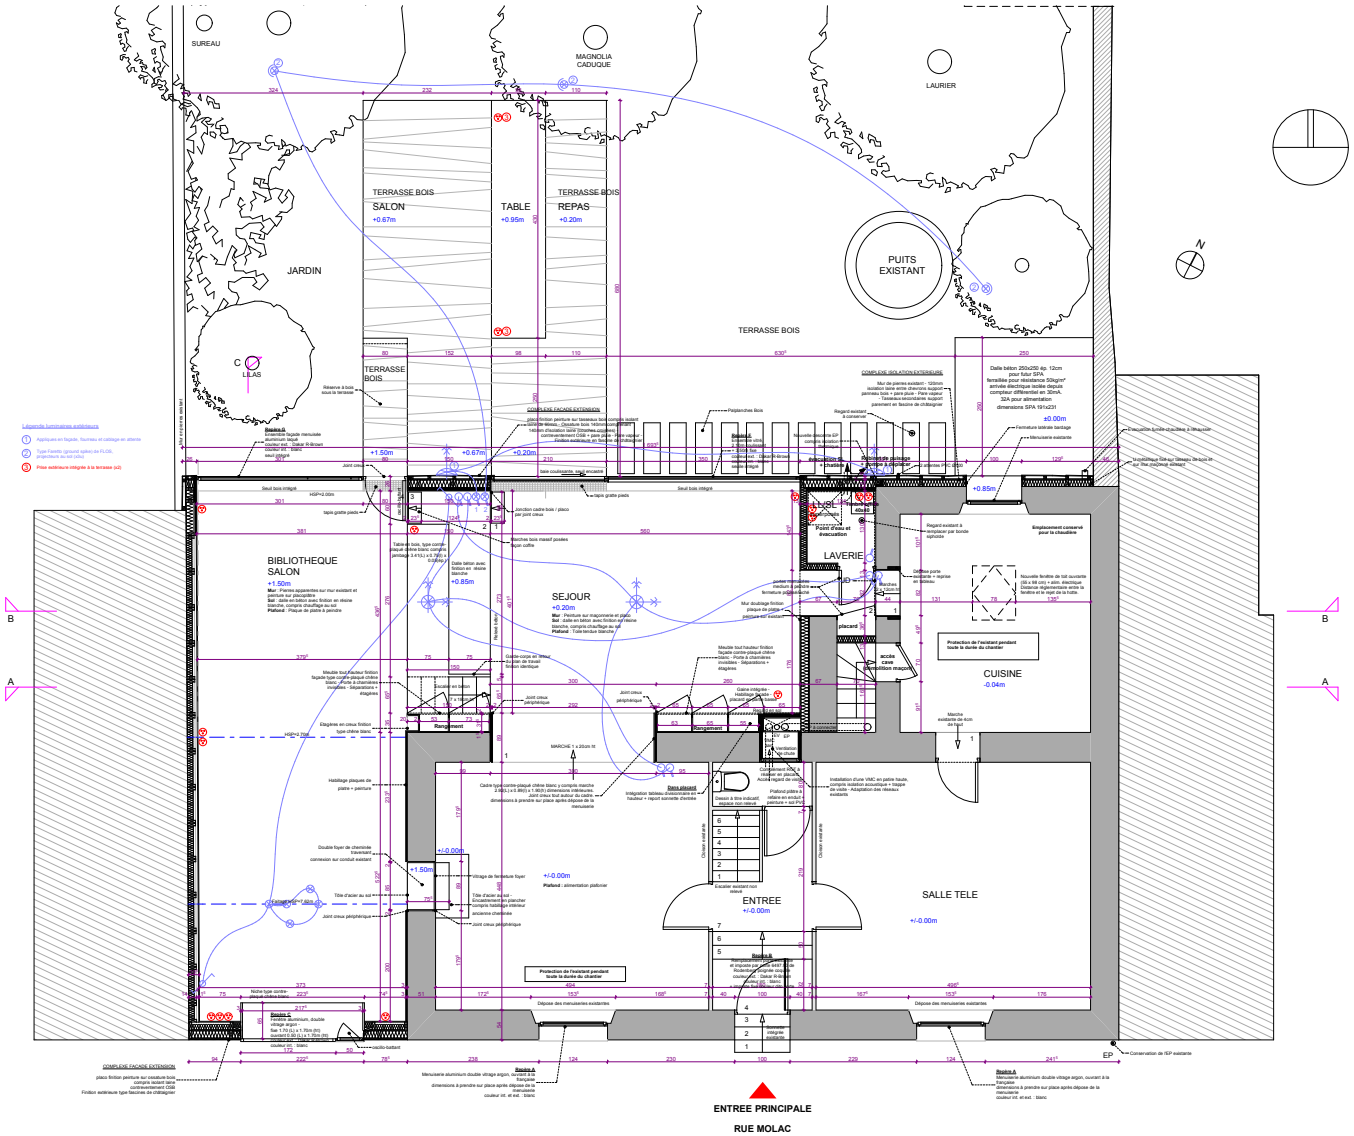

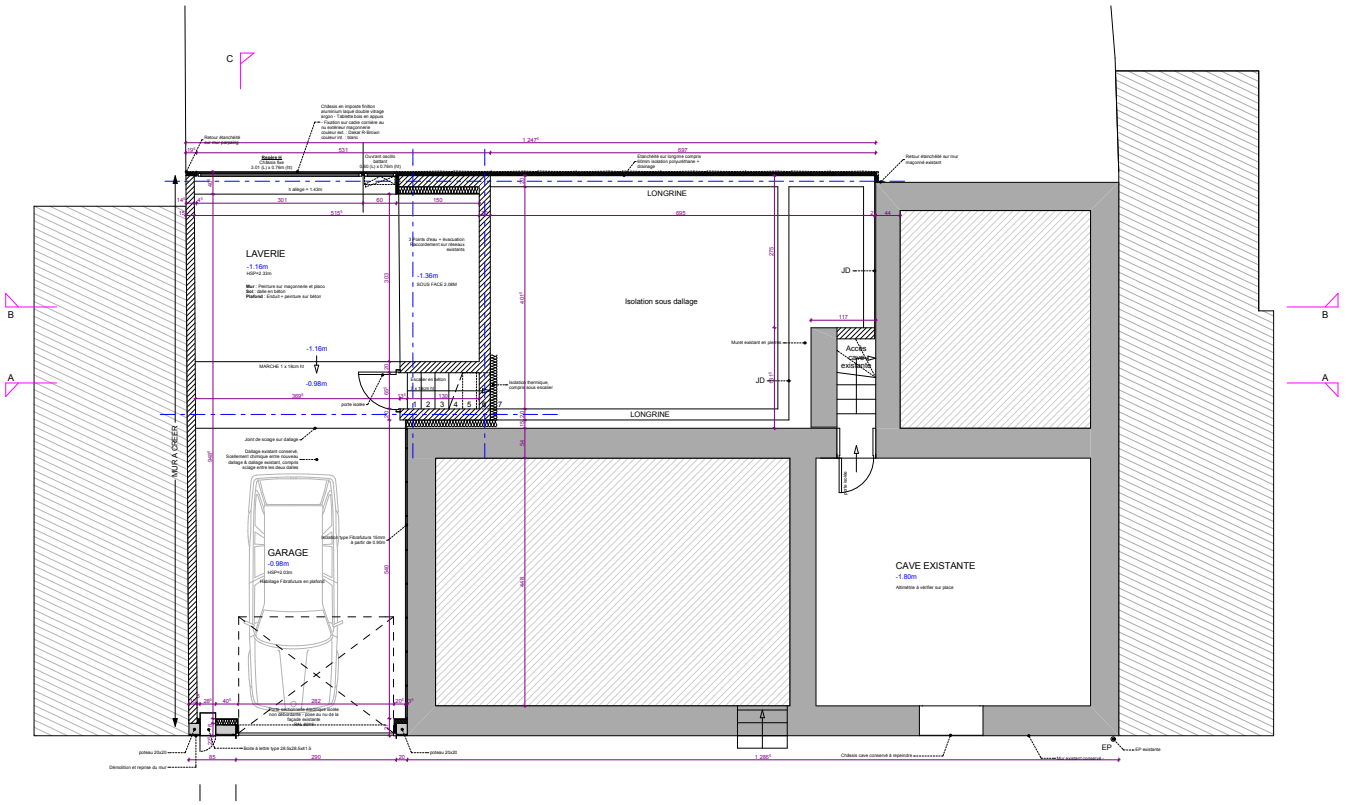

FACADE SUD (Rue Molac)

EXTENSION MAISON MOLAC

PLANS RDC / R-1

N° AFFAIRE	ARCHITECTE	DATE	ECHELLE	NUMERO PLAN
AN 43411	FORMA6	24.01.2014	1/50	601

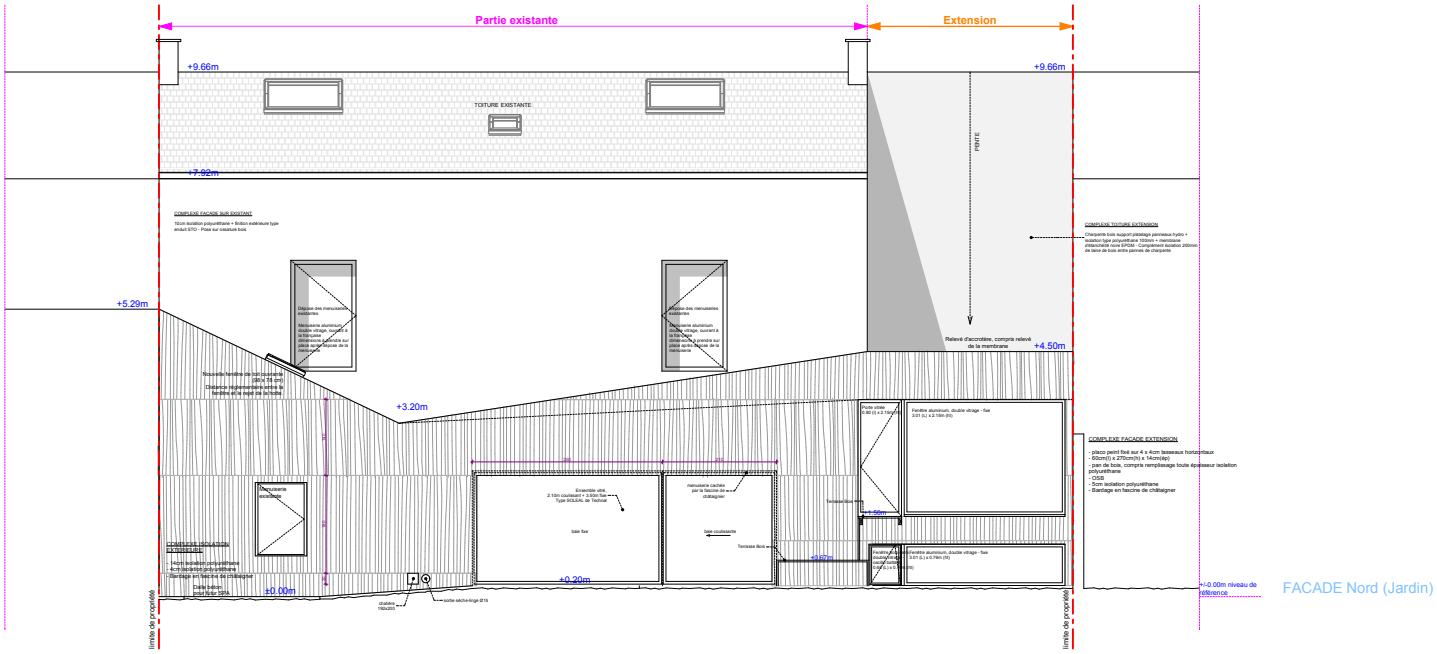

FACADE Nord (Jardin)

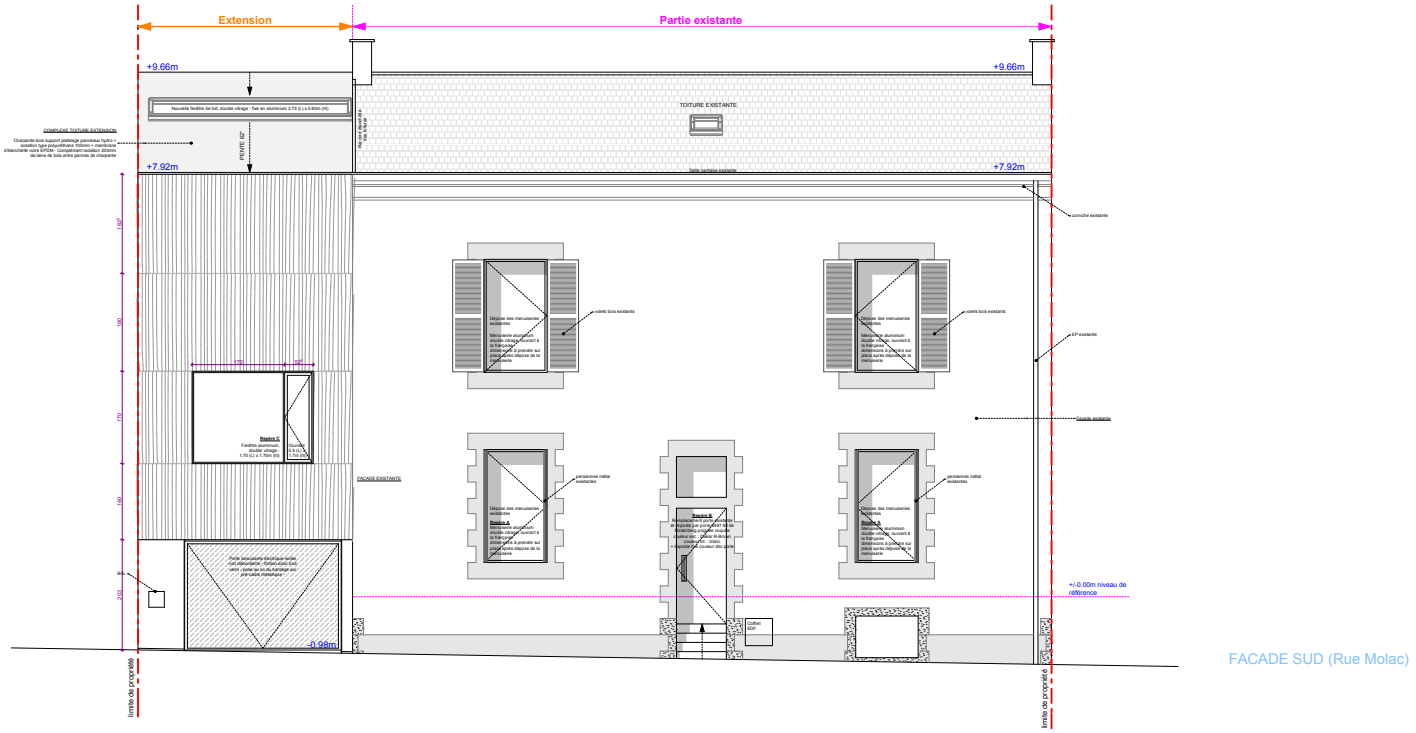

FACADE SUD (Rue Molac)

EXTENSION MAISON MOLAC

FACADES

N° AFFAIRE	ARCHITECTE	DATE	ECHELLE	NUMERO DU PLAN
AN 43411	FORMA6	24.01.2014	1/50	602

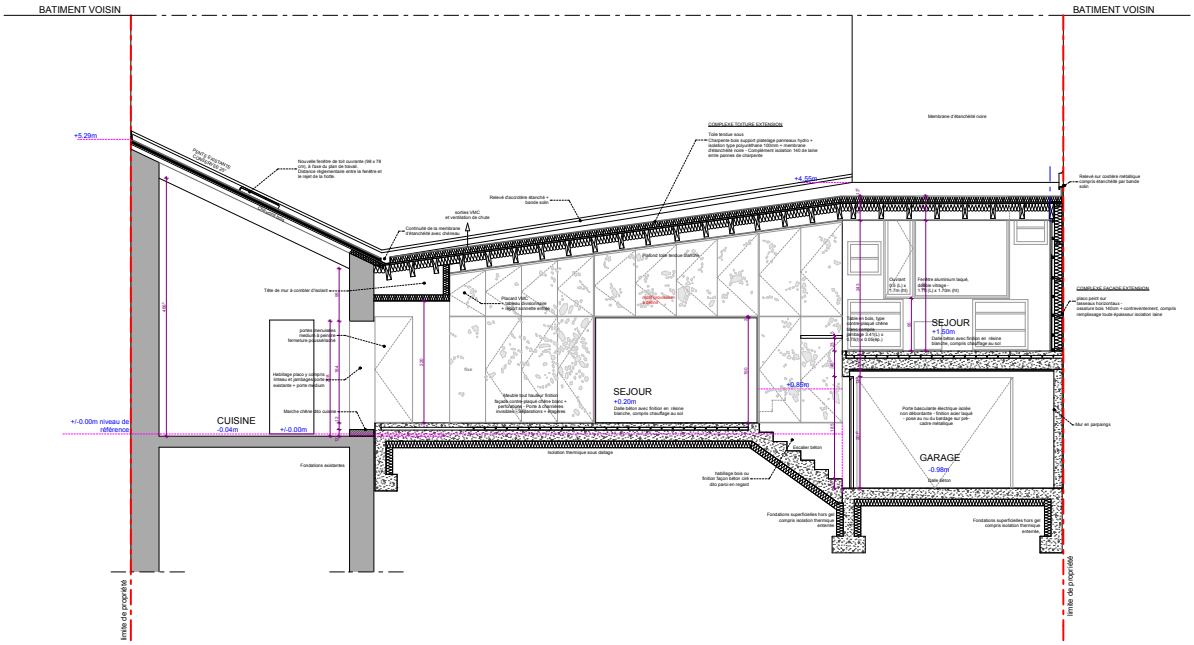

COUPE AA

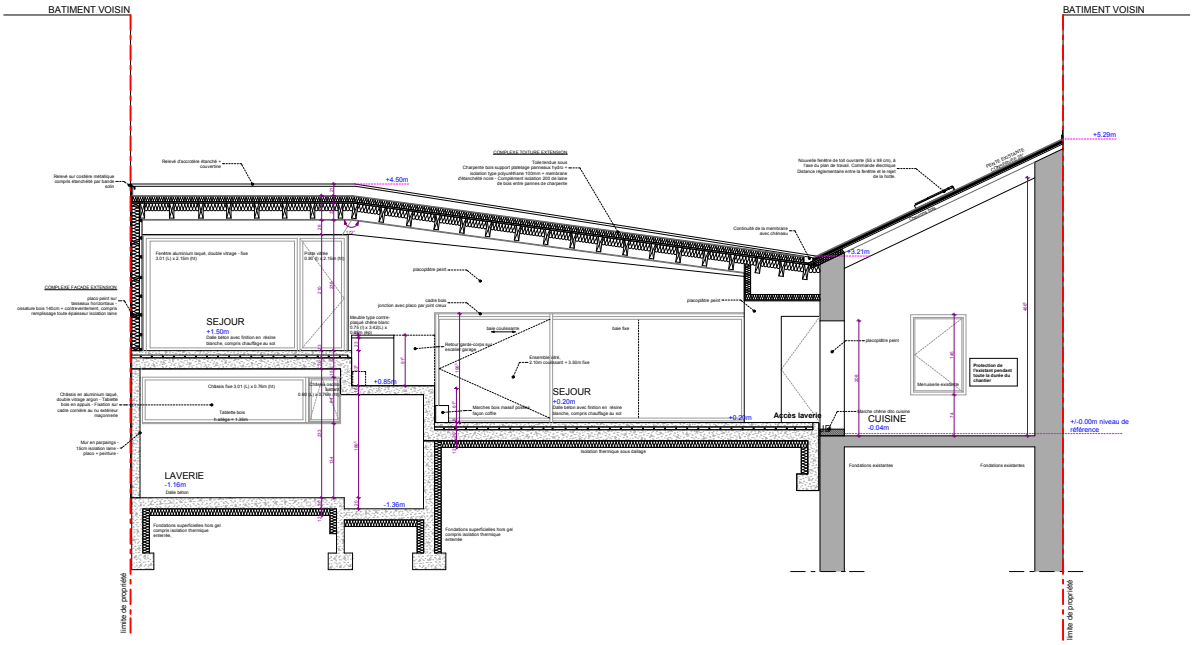

COUPE BB

EXTENSION MAISON MOLAC

COUPE AA/BB

N° AFFAIRE	FORMAT PLAN	DATE	ECHELLE	NUMERO PLAN
AN 43411	FORMA6	24.01.2014	1/50	604

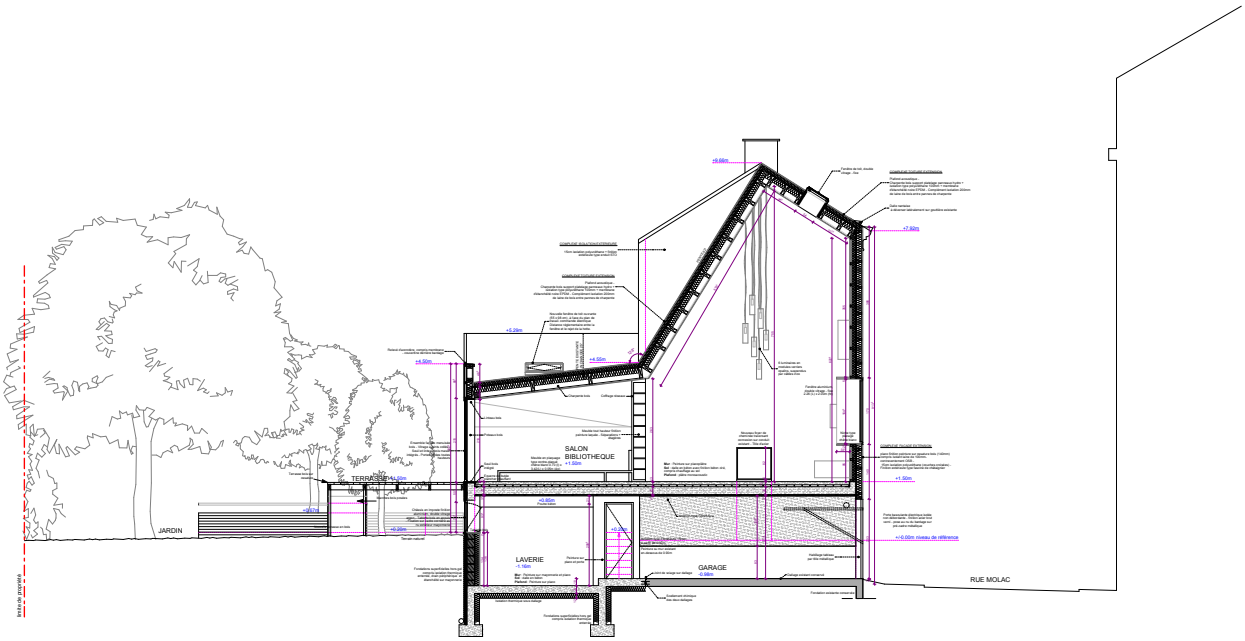

EXTENSION MAISON MOLAC

COUPE CC

AN 43411	FORMA6	24.01.2014	1/50	605